


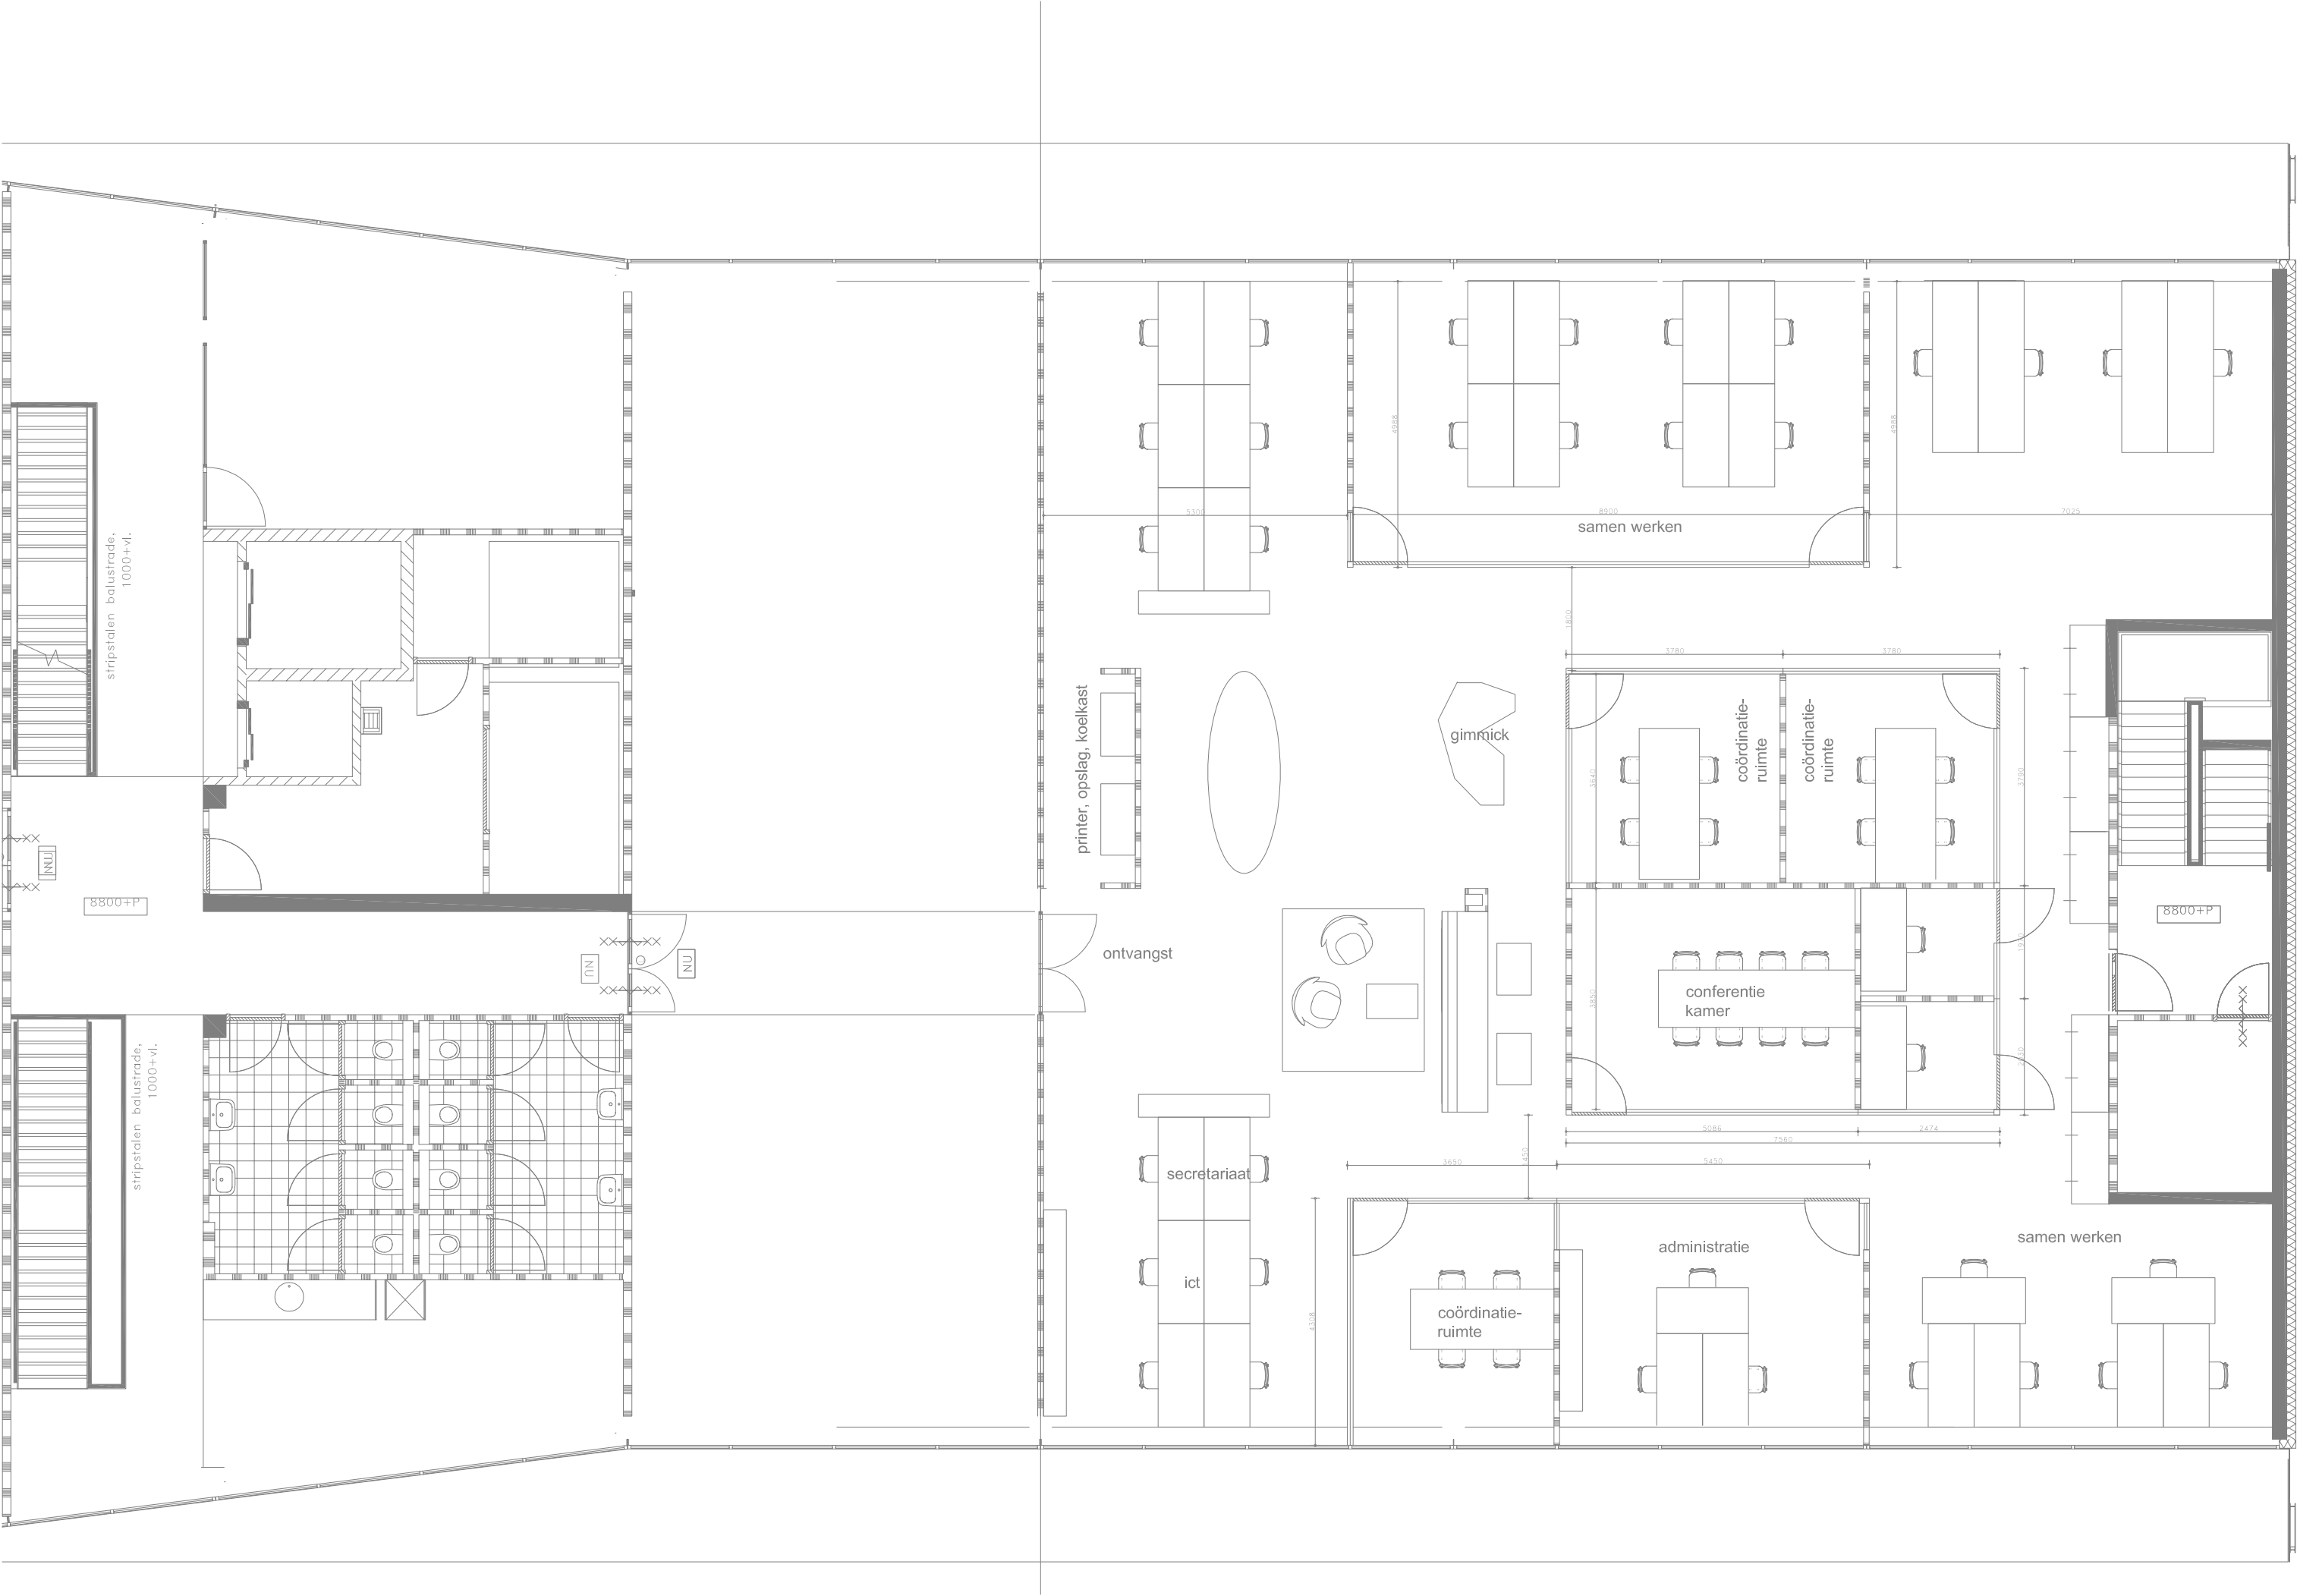

project	: Brightlands gebouwen X en Y	opdrachtgever	: Brightlands
projectnummer	: 2016.032	architect	: Van Den Pauwert Architecten BNA

omschrijving

datum	: 11-2-19	gewijzigd:
formaat	: A2	a:
schaal	: 1:100	b:
getekend	: GV	c:
gezien	: WB	d:
datum onderlegger	: 24-10-2108	e:

T: 088-0322222
E: info@huygen.net
W: www.huygen.net

VL HIA